


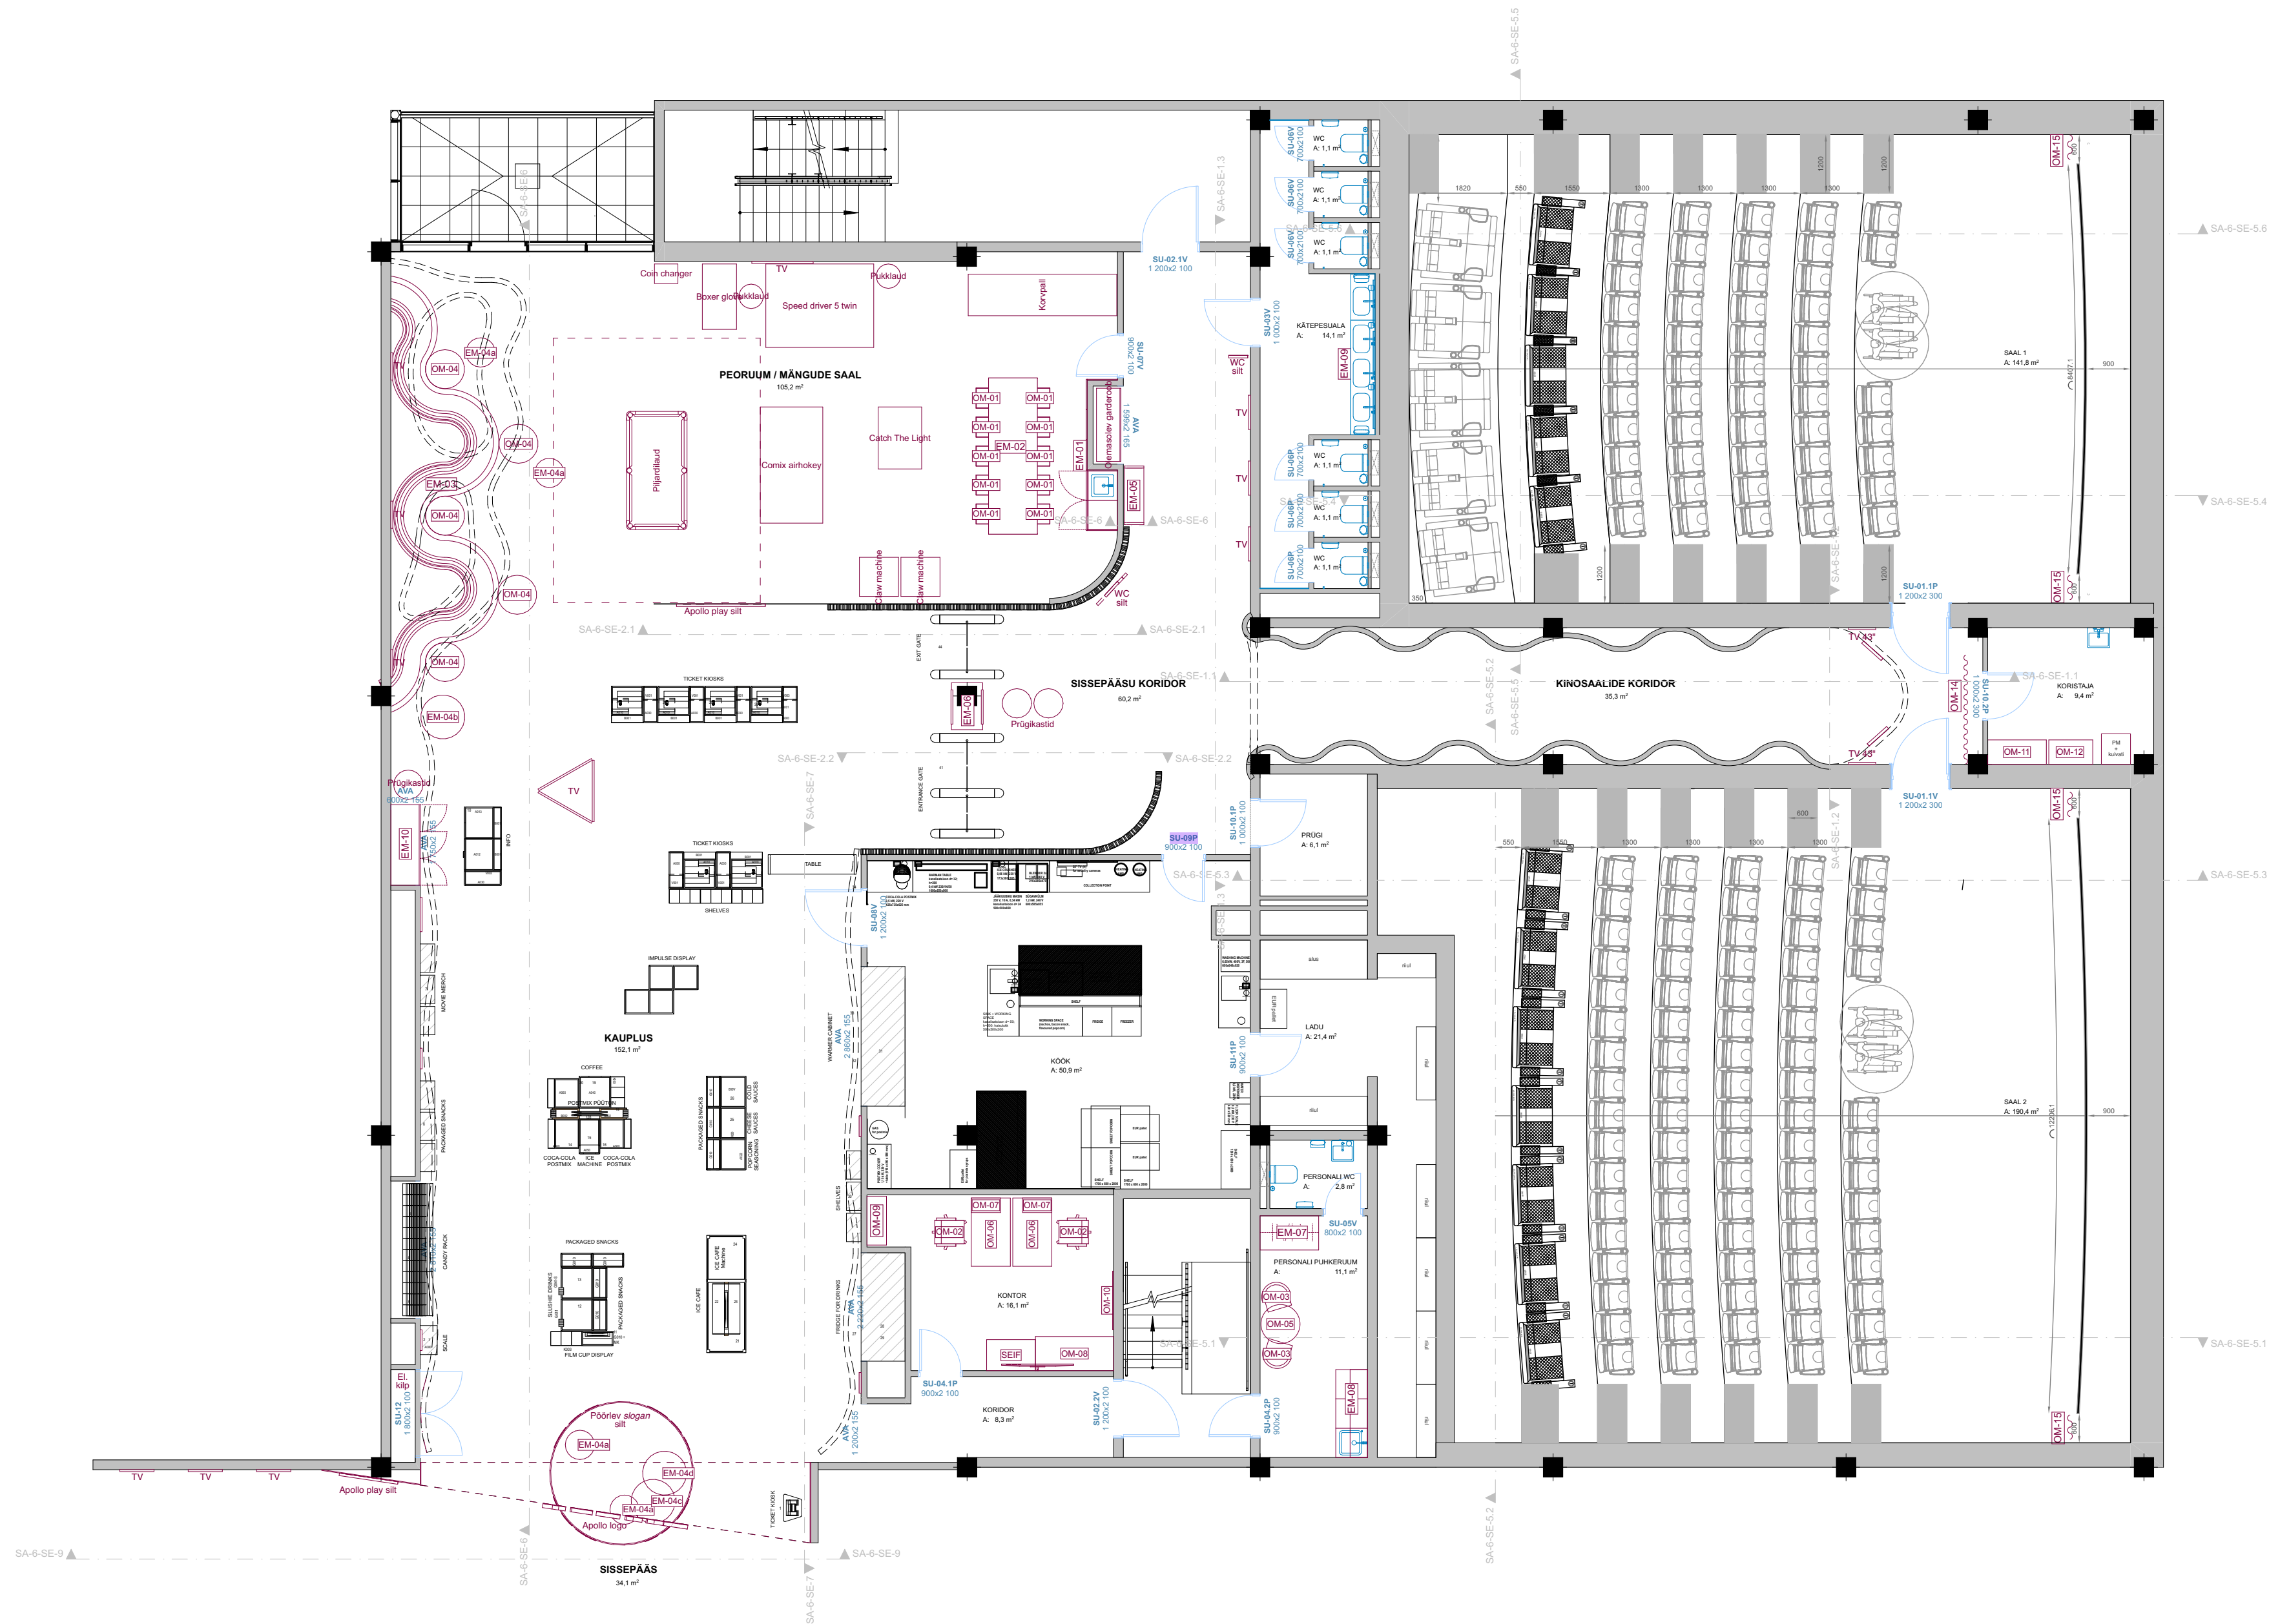

- Kõik mõõdud täpsustada objektil!
- Joonist vaadata koos teiste eriosade projektilahendustega. Erinevuste korral konsulteerida sisearhitektiga.
- Antud joonis on kujujoonis ning ei ole tootmise aluseks. Konstruktsiooni täpne lahendus teostajalt, kes võib täiustada konstruktsiooni või lahendust selliselt, et üldilme ei muutu. Toote/lahenduse vastupidavuse, turvalisuse ja töökindluse tagab valmistaja. Muudatused kooskõlastada sisearhitektiga.
- Tooted paigaldada tootja/tarnija juhiste järgi.
- Töövõtja kontrollarvutab seadmete/toodete kogused, kompleksuse jms aspektid.

Antud joonis tühistab kõik varasema kuupäevaga joonised.

	PROJEKTEERIA Ann Press-Kulmats, Mari Jõemägi, Skaidrite Kits LAVI EESPROJEKTEERIMINE LAVI EES INFO@LAVI.EE 5648 8013	PROJEKT Apollo Cinema Kella ADDRESS Kella FORMAAT / MÕÕTKA A2 / 1:100	JOONISE NR. SA-5.1.1 KUIPÄEV 29.09.2025 STADIUM PP	JOONIS Mööbliplaan 1. korrus