
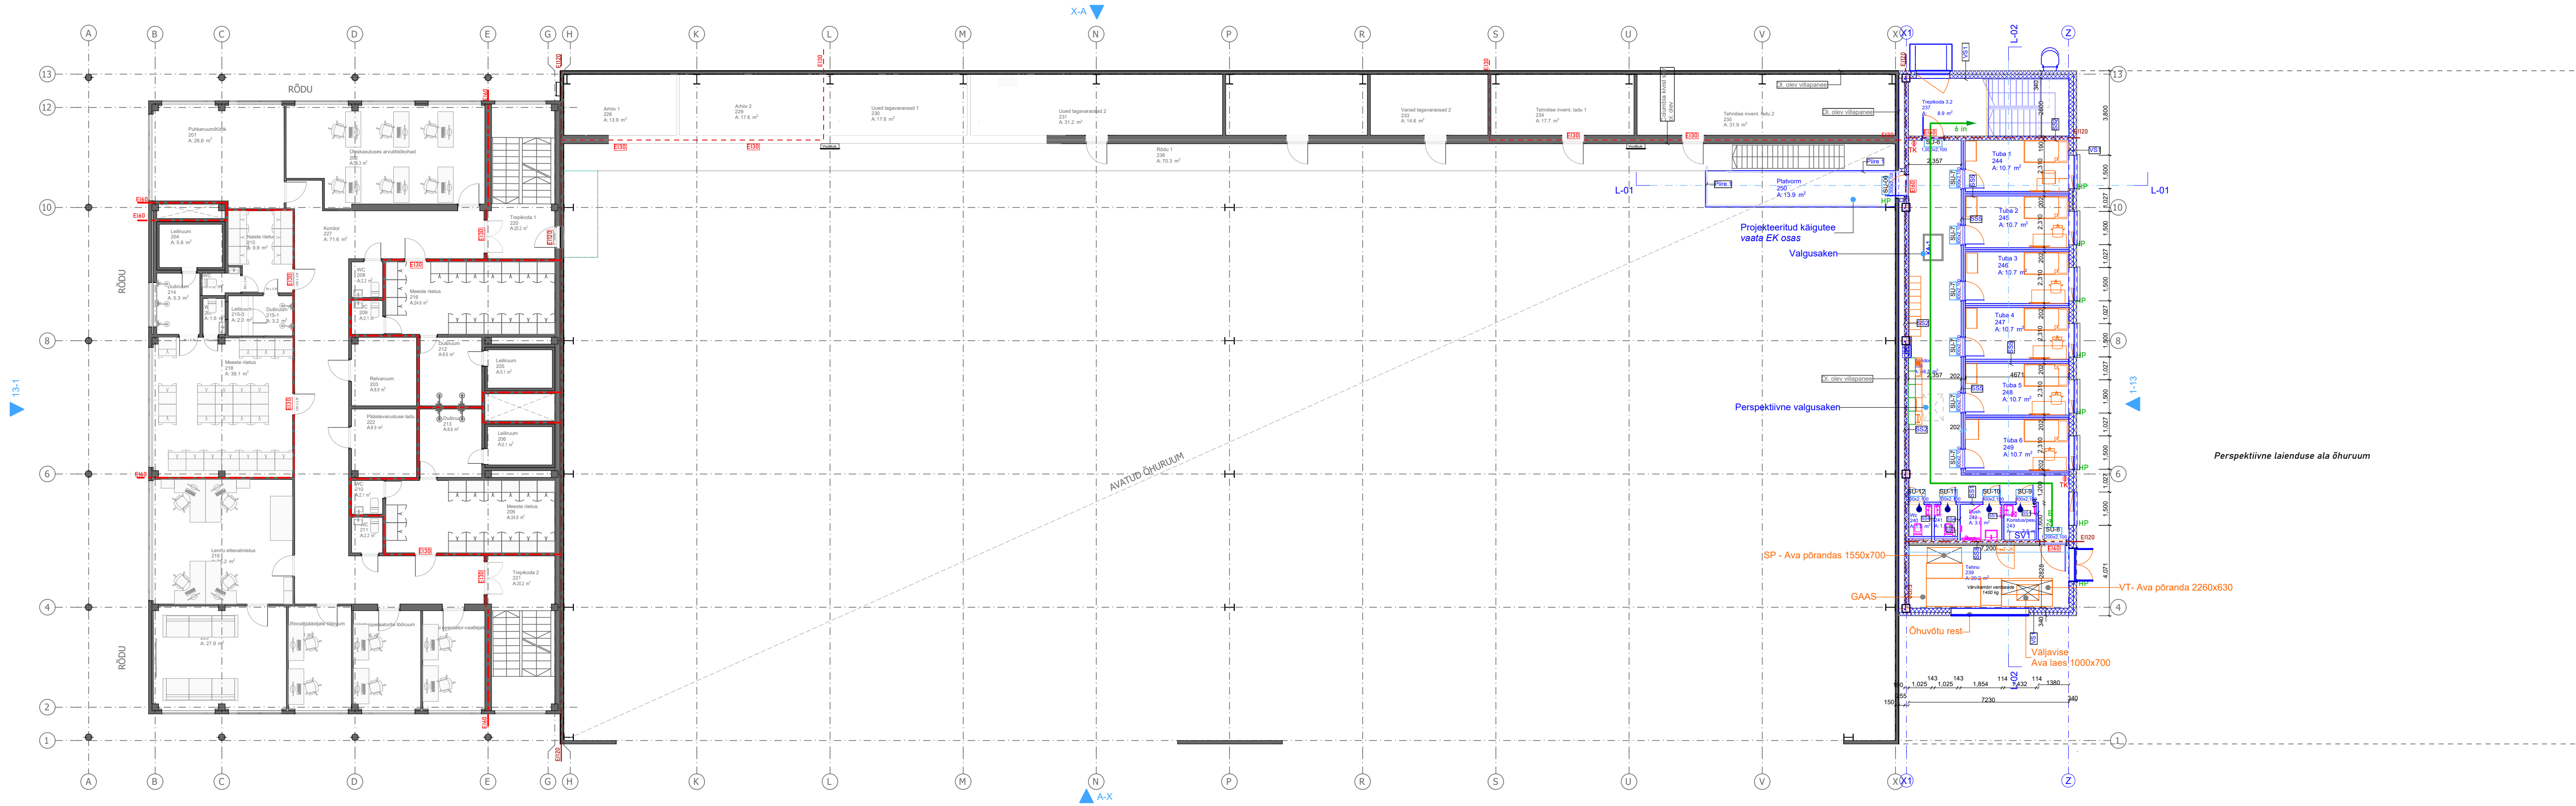


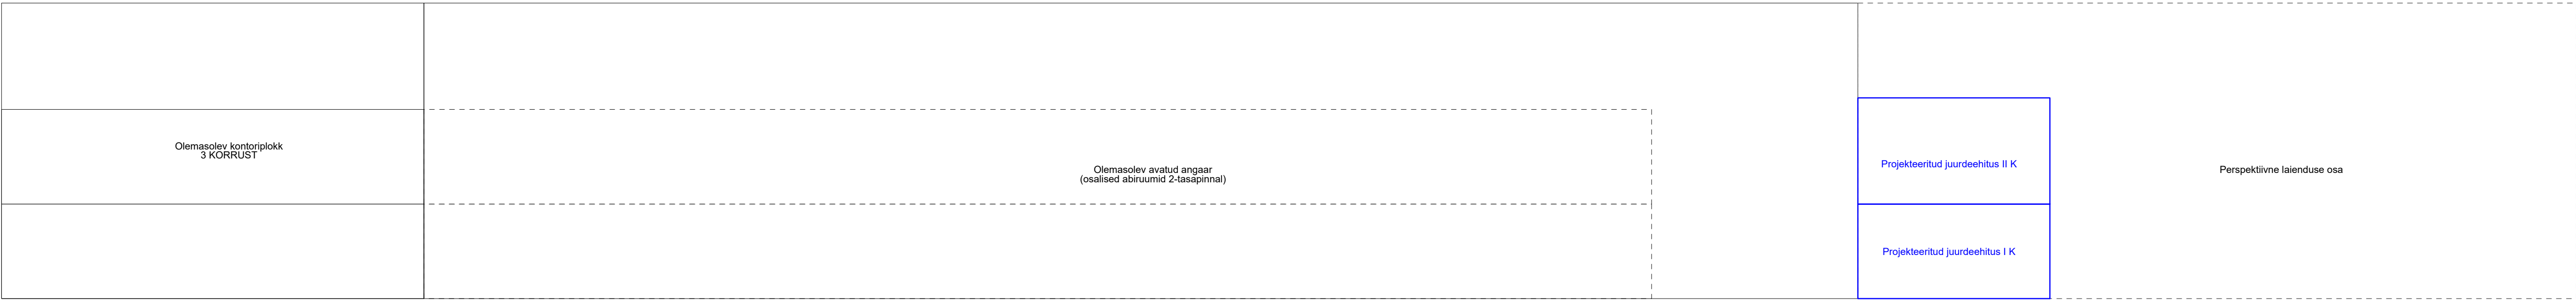

- TINGMÄRGID**
- E120 - E120 tulestiksekskeksioon
  - E160 - E160 tulestiksekskeksioon
  - E130 - E130 tulestiksekskeksioon
  - E150 - Tulestiksekskeksiooni avatide (number näitab tulestiksekskeksiooni)
  - E150 - Konstruktsioonitööbahi tähtis
  - E150 - Planeeritav mööbel/tehnoloogia (lahendatakse eraldi)
  - E150 - Evakuatsioon / väljumistee
  - HP - Hüdralaiajapääs
  - TK - Tulekustuti asukoht
  - GAAS - Gaasimõõde süm
  - SV1/2 - Ventilatsioon seade
  - JK - Jootuskiip
  - Märgruumi nöötele vastav sisekliima (materjalide valikul)

Joonist lugeda värvilisena. Joonise värvide põhimõte:  
Sinine värvikasutus = uued ja muudetavad lahendused  
Hall ja must värvikasutus = olemasolev olukord

Märkused:  
1) Konstruktsioonitööbahi on kirjeldatud joonisel AR-8-02 ja EK osas  
2) Ruumide ekvivalentsid on toodud AR-8-01  
3) Suitsueemalduse plaan on esitatud eraldi

**MÄRKUSED:**  
Joonise alusena on kasutatud Ehitusinsener OÜ (reg 12481341) poolt koostatud Lennutehnika angaari laiendamise ehitusprojekti (töö nr 24048) PP staadiumis jooniseid.

**ASUTUSESISESEKS KASUTAMISEKS:**  
Märge tehtud: 06.03.2025  
Kehtib kuni: 06.03.2030  
Alus: AvTS § 35 lg 1 p 9, 10  
Teabevaldaja: Politsei- ja Piirivalveamet

**RESHAPE.**

RESHAPE OÜ | Regikood 16244878 | www.reshape.ee | info@reshape.ee

PROJEKT  
LENNUTEHNIKA ANGAARI LAIENDAMINE

AADRES  
VAIKE-SÕJAMAE 22A, LASNAMÄE, TALLINN, HARJU MAAKOND

TELLUJA  
RIIGI KINNISVARA AS

ARVUTUS  
SAAMUEL RAMMO

JOONIS  
2. KÖRRUST

STAADIUM  
TOOPROJEKT

YBID  
A05032501

HOOTIKAVA  
1:150

FORMAAT  
594x841

KUUPÄEV  
15/03/2025

JOONISE NR  
AR-5-02

YKATUTAV ARVUTUS  
TAURI TAMME