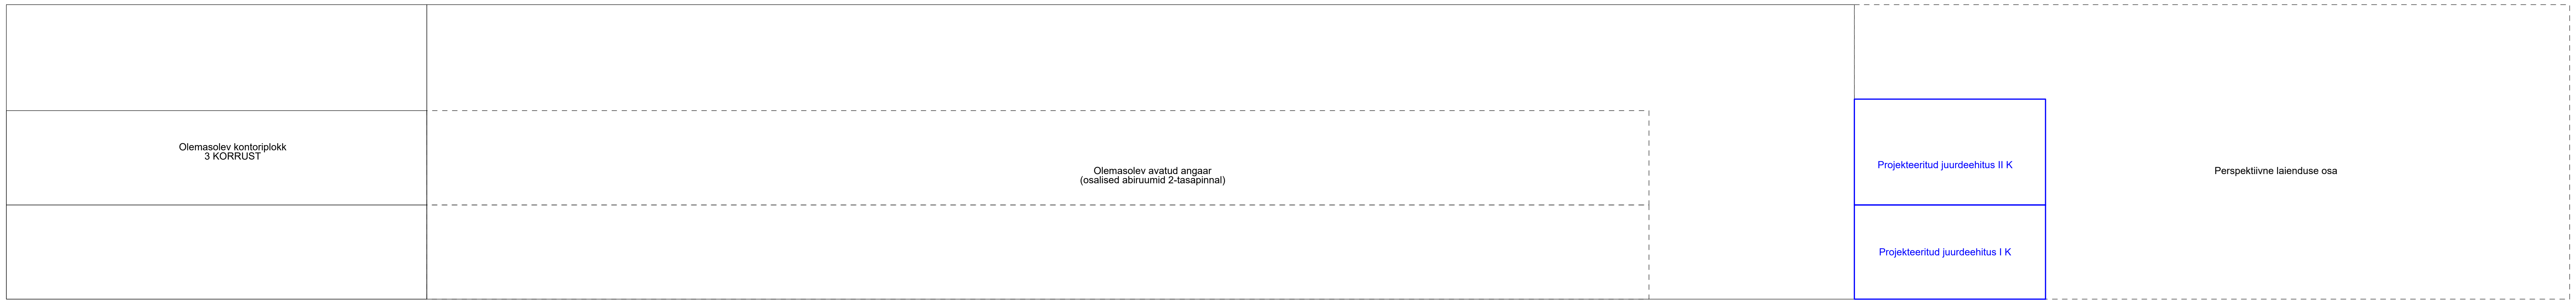
Olemasolev kontoriplokk
3 KORRUST
Olemasolev avatud angaar
(osalised abiruumid 2-tasapinnal)
Projekteeritud juurdeehitus II K
Projekteeritud juurdeehitus I K
Perspektiivne laienduse osa


PÄ SISENEMINE
X-A
A-X
13-1
1-13
Katlaruum 101 A: 22.3 m²
Kompressor 102 A: 9.1 m²
SLJK-1.2
ATS
Valveseadmed 104 A: 12.2 m²
Puhkeruum 105 A: 13.5 m²
Diiselgeneraator 103 A: 15.8 m²
GENERAATOR
Trepikoda 1 106 A: 51.1 m²
Veemõõdusõlm 107 A: 12.0 m²
PJK
Elektrikilp 108 A: 5.6 m²
Koristusvahendid 110 A: 4.9 m²
Leiliruum 111 A: 3.9 m²
WC 112 A: 2.5 m²
Duširuum 114 A: 5.5 m²
WC 113 A: 2.2 m²
Töökoda 109 A: 20.3 m²
Riietus 117 A: 6.3 m²
Mõõteriistade labor 116 A: 17.7 m²
Koridor 119 A: 31.4 m²
Tehnikute garderoob 115 A: 30.6 m²
Raadiolabor 120 A: 18.3 m²
Elektrilabor 118 A: 6.9 m²
Tehnilise eskadrilli brifing 123 A: 20.4 m²
Ekraaniga labor 122 A: 8.1 m²
SLJK ANGAAR
Garaaž 121 A: 65.1 m²
Trepikoda 2 124 A: 51.1 m²
SEJ
SLJK-1.1
ME-SE 1.3 1.4
Tehnilise eskadrilli puhkeruum/köök 125 A: 26.3 m²
Akuruum 1 126 A: 11.5 m²
Akuruumi abiruum 127 A: 9.5 m²
Akuruum 2 128 A: 12.0 m²
Määrdeainete ladu 129 A: 11.9 m²
Ladu 130 A: 13.8 m²
Tööriistaladu 131 A: 32.5 m²
Lennukite eskadrilli varustus 132 A: 24.3 m²
Päästeülikondade pesu- ja kuivatusruum 134 A: 24.5 m²
Kopterite eskadrilli varustus 135 A: 84.0 m²
Columbia kivist sein ol. olev
Ol. olev villapanee
JK1.4
L-01
L-02
Lennutehnika angaar 133 A: 1,548.0 m²
Voolikuk.
EI120
EI60
EI30
8,015
800
960
Katuseredel R-1
16 in
VS1
VR3
VR2
VU-2 1,000x2,300
Trepikoda 3.1 136 A: 13.1 m²
Ladu 143 A: 3.8 m²
WC 142
SU-1
SV2
SU-14 900x2,100
SS2
Ladu 137 A: 45.3 m²
1,200
5840
1.190
0.890
SL-1
10,553
TV-1 2,500x2,300
TK
Ladu 138 A: 58.7 m²
SU-3 2,000x2,300
1,500
2,703
24,530
8,039
22,625
30,300
4,000
7,000
330 mm põrand
6050
8,894
Lüüs 140 A: 4.2 m²
SS1
SU-4
Abiruum 141 A: 5.7 m²
SU-2
VU-1 900x2,300
GAAS
VS
1,805
900
5,310
3,65 x 3,00
10 in
720.6 m²
A B C D E G H K L M N P R S U V X X1 Z
13 12 10 8 6 4 2 1

TINGMÄRGID

EI120	EI120 tulətõkkesektsioon
EI60	EI60 tuletõkkesektsioon
EI30	EI30 tuletõkkesektsioon
EI60	Tuletõkke avatäide *(number näitab tulepüsivust minutites)*
SS2	Konstruktsioonitüübi tähis
▭	Planeeritav mööbel/tehnoloogia (lahendatakse eraldi)
→	Evakuatsioon / väljumistee
HP	Hädaväljapääs
TK	Tulekustuti asukoht
GAAS	Gaasimõõte sõlm
SV1/2	Ventilatsiooni seade
JK	Jaotuskilp
💧	Märgruumi nõuetele vastav sisekliima (materjalide valikul)

Joonist lugeda värvilisena. Joonise värvide põhimõte:

Sinine värvikasutus = uued ja muudetavad lahendused
Hall ja must värvi kasutus = olemasolev olukord

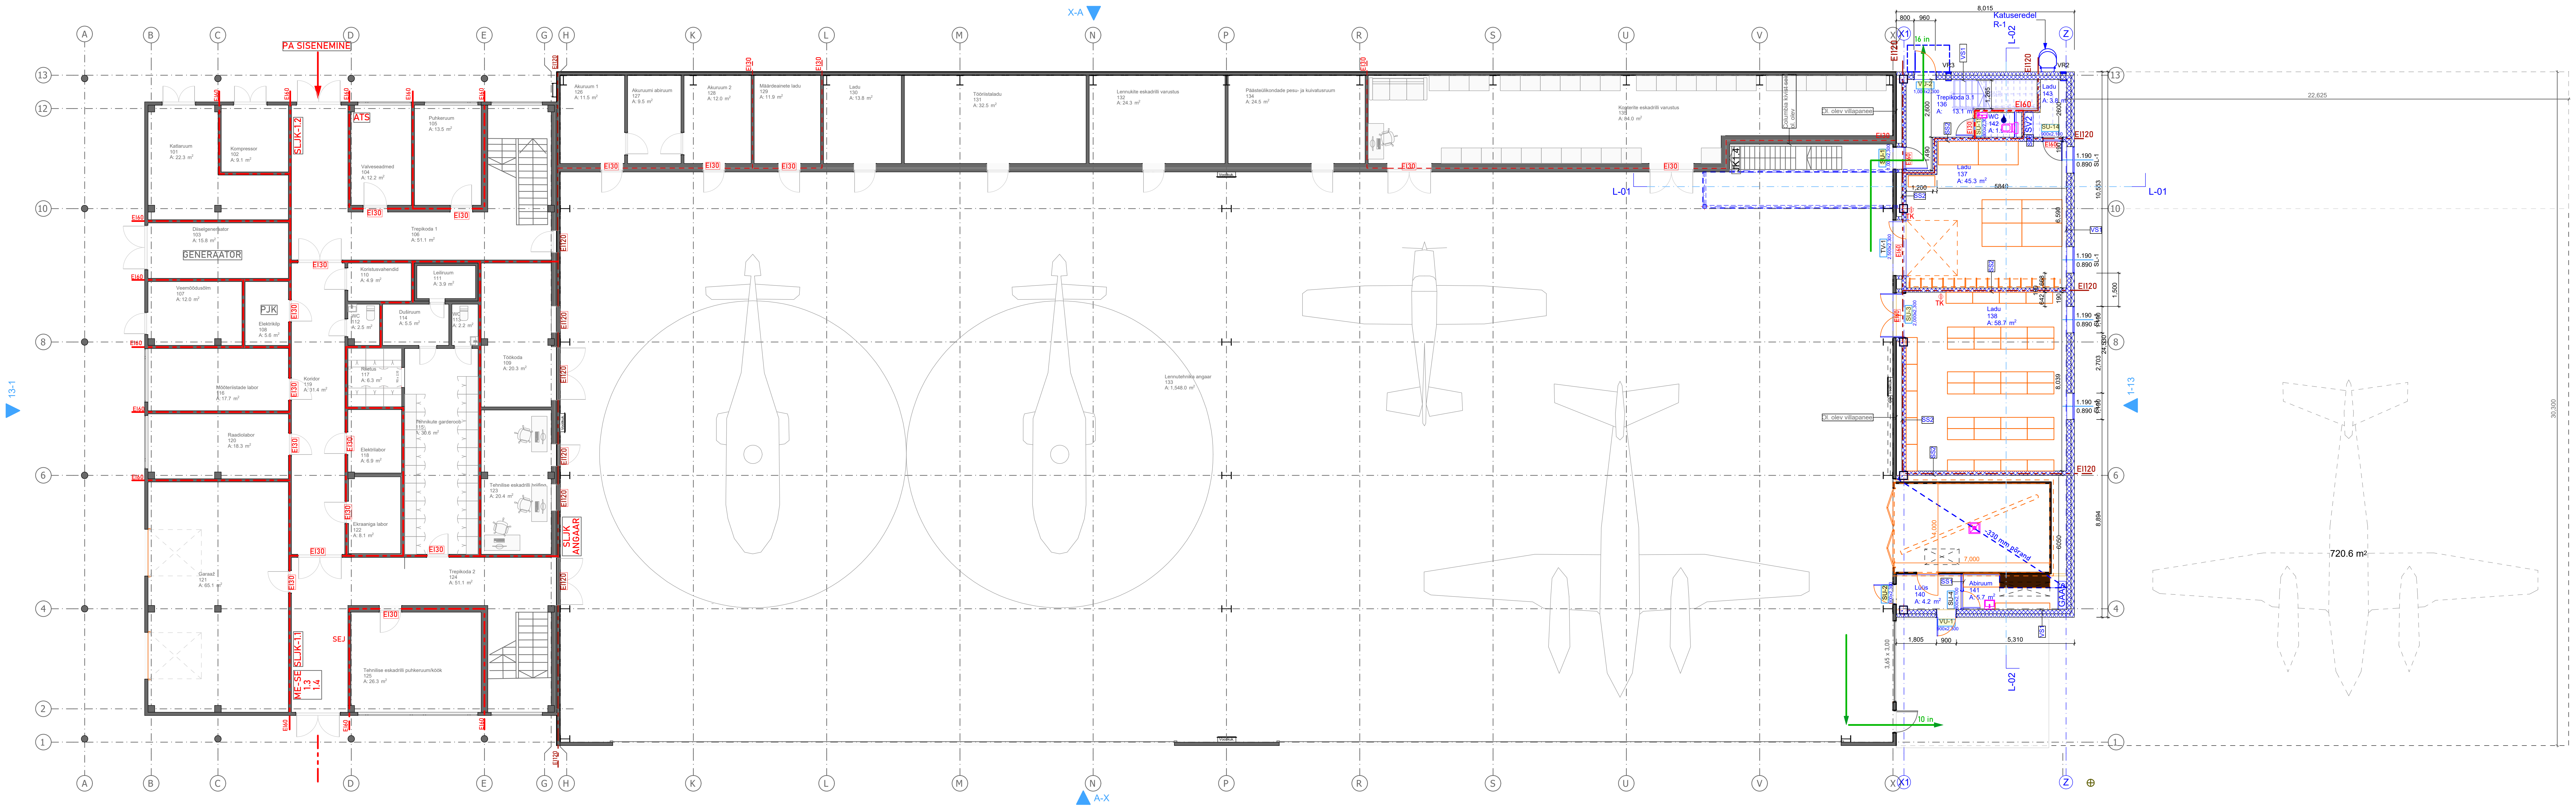Märkused:
1) Konstruktsioonitüübid on kirjeldatud joonisel AR-8-02 ja EK osas
2) Ruumide eksplikatsioonid on toodud AR-8-01
3) Suitsueemalduse plaan on esitatud eraldi

MÄRKUSED:
Joonise alusena on kasutatud Ehitusinsener OÜ (reg 12481341) poolt koostatud Lennutehnika angaari laiendamise ehitusprojekti (töö nr 24048) PP staadiumis jooniseid.

ASUTUSESISESEKS KASUTAMISEKS:
Märge tehtud: 06.03.2025
Kehtib kuni: 06.03.2030
Alus: AvTS § 35 lg 1 p 9, 10
Teabevaldaja: Politsei- ja Piirivalveamet

RESHAPE.
RESHAPE OÜ | rg-kood 16246878 | www.reshape.ee | info@reshape.ee

PROJEKT LENNUTEHNIKA ANGAARI LAIENDAMINE	
AADRESS VÄIKE-SÕJAMÄE 22A, LASNAMÄE, TALLINN, HARJU MAAKOND	
TELLIJA RIIGI KINNISVARA AS	
ARHITEKTID SAAMUEL RAMMO	VASTUTAV ARHITEKT TAURI TAMME
JOONIS 1. KORRUS	
STAADIUM TÖÖPROJEKT	FORMAAT 594x841
TÖÖ NR. A05032501	KUUPÄEV 15/03/2025
MÕÕTKAVA 1:150	JOONISE NR. AR-5-01