Olemasolev kontoriplokk 3 KORRUST	Olemasolev avatud angaar (osalised abiruumid 2-tasapinnal)	Projekteeritud juurdeehitus II K Projekteeritud juurdeehitus I K

Perspektiivne laienduse osa

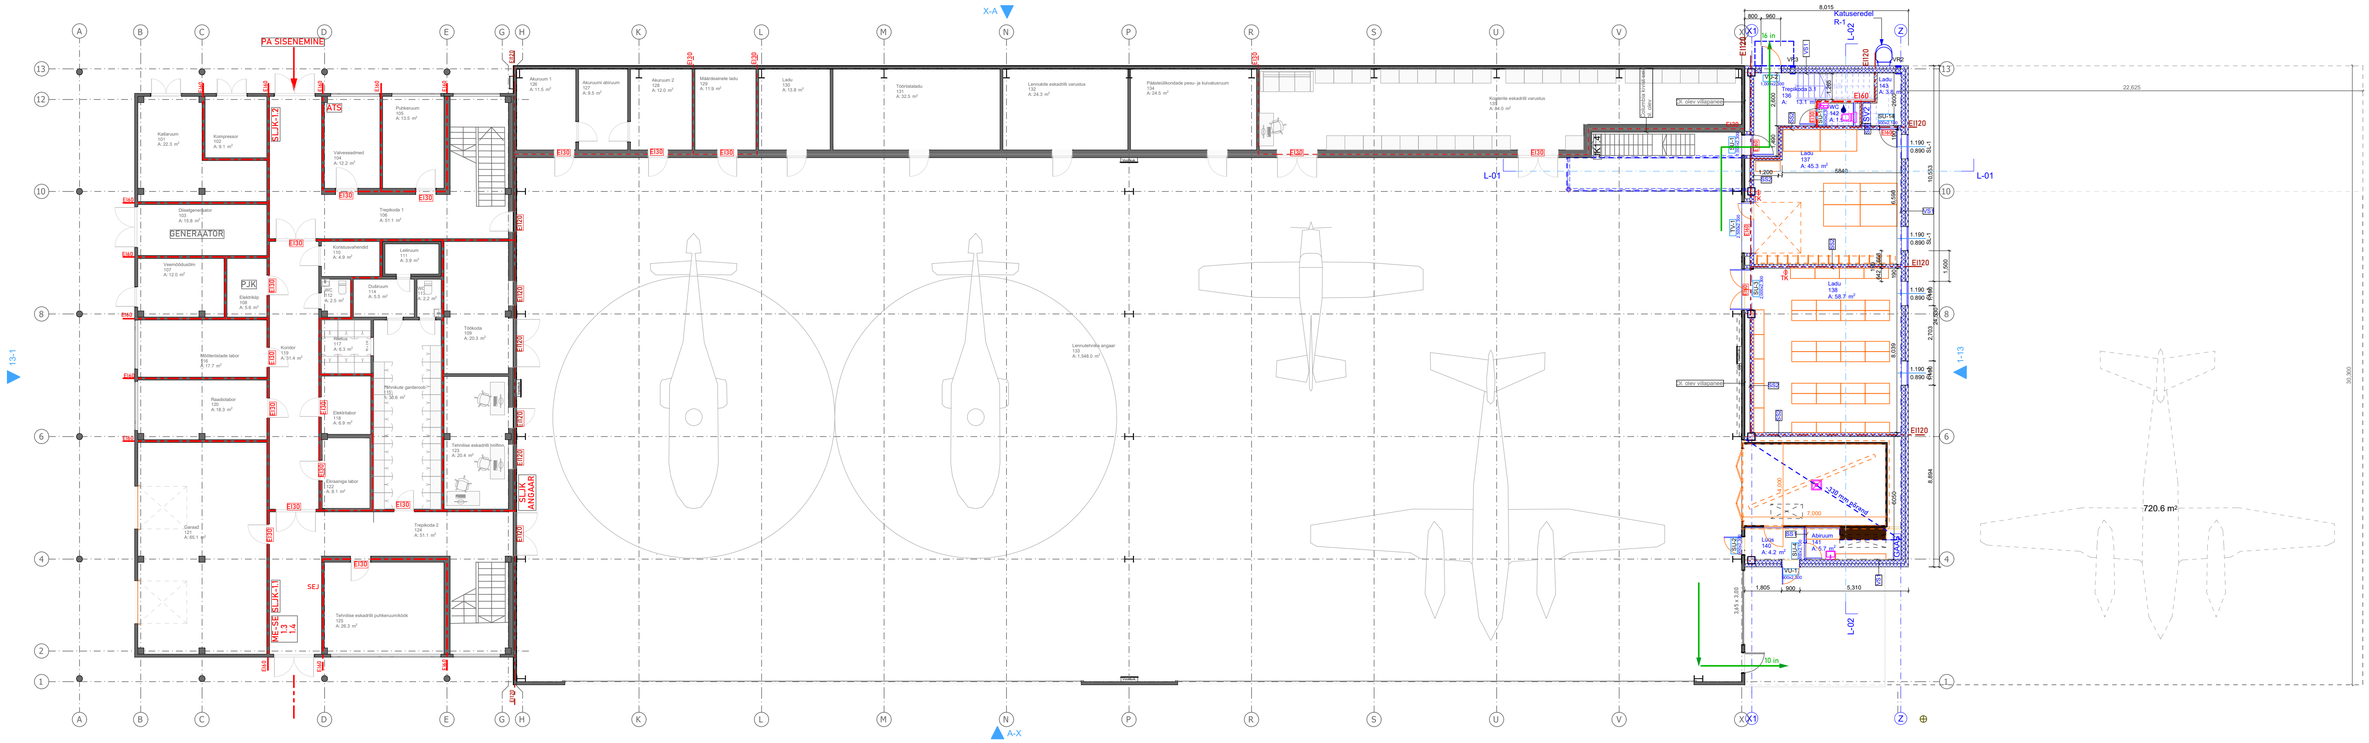

TINGMÄRGID

- EI120 — EI120 tuletõkkesektsioon
- EI60 — EI60 tuletõkkesektsioon
- EI30 — EI30 tuletõkkesektsioon
- EI30 Tuletõkke avatäide *(number näitab tulepüsivust minutites)*
- K53 Konstruktsioonitüübi tähis
- Planeeritav mööbel/tehnoloogia (lahendatakse eraldi)
- Evakuatsioon / väljumistee
- HP Hädaväljapääs
- TK Tulekustuti asukoht
- GAAS Gaasimõõte sõlm
- SV1/2 Ventilatsiooni seade
- JK Jaotuskilp

Märgruumi nõuetele vastav siseklliima (materjalide valikul)

Joonist lugeda värviliisena. Joonise värvide põhimõte:

Sinine värvikasutus = uued ja muudetavad lahendused
Hall ja must värvi kasutus = olemasolev olukord

Märkused:
1) Konstruktsioonitüübid on kirjeldatud joonisel AR-8-02 ja EK osas
2) Ruumide eksplikatsioonid on toodud AR-8-01
3) Suitsueemalduse plaan on esitatud eraldi

MÄRKUSED:

Joonise alusena on kasutatud Ehitusinsener OÜ (reg 12481341) poolt koostatud Lennutehnika angaari laiendamise ehitusprojekti (töö nr 24048) PP staadiumis jooniseid.

ASUTUSESISESEKS KASUTAMISEKS:
Märge tehtud: 06.03.2025
Kehtib kuni: 06.03.2030
Alus: AvTS § 35 lg 1 p 9, 10
Teabevaldaja: Politsei- ja Piirivalveamet

RESHAPE.

RESHAPE OÜ | rg-kood 16246878 | www.reshape.ee | info@reshape.ee

PROJEKT LENNUTEHNIKA ANGAARI LAIENDAMINE	
AADRESS VÄIKE-SÕJAMÄE 22A, LASNAMÄE, TALLINN, HARJU MAAKOND	
TELLIJA RIIGI KINNISVARA AS	
ARHITEKTID SAAMUEL RAMMO	VASTUTAV ARHITEKT TAURI TAMME
JOONIS 1. KORRUS	
STAADIUM TÖÖPROJEKT	FORMAAT 594x841
TÖÖ NR. A05032501	KUUPÄEV 15/03/2025
MÕÕTKAVA 1:150	JOONISE NR. AR-5-01