


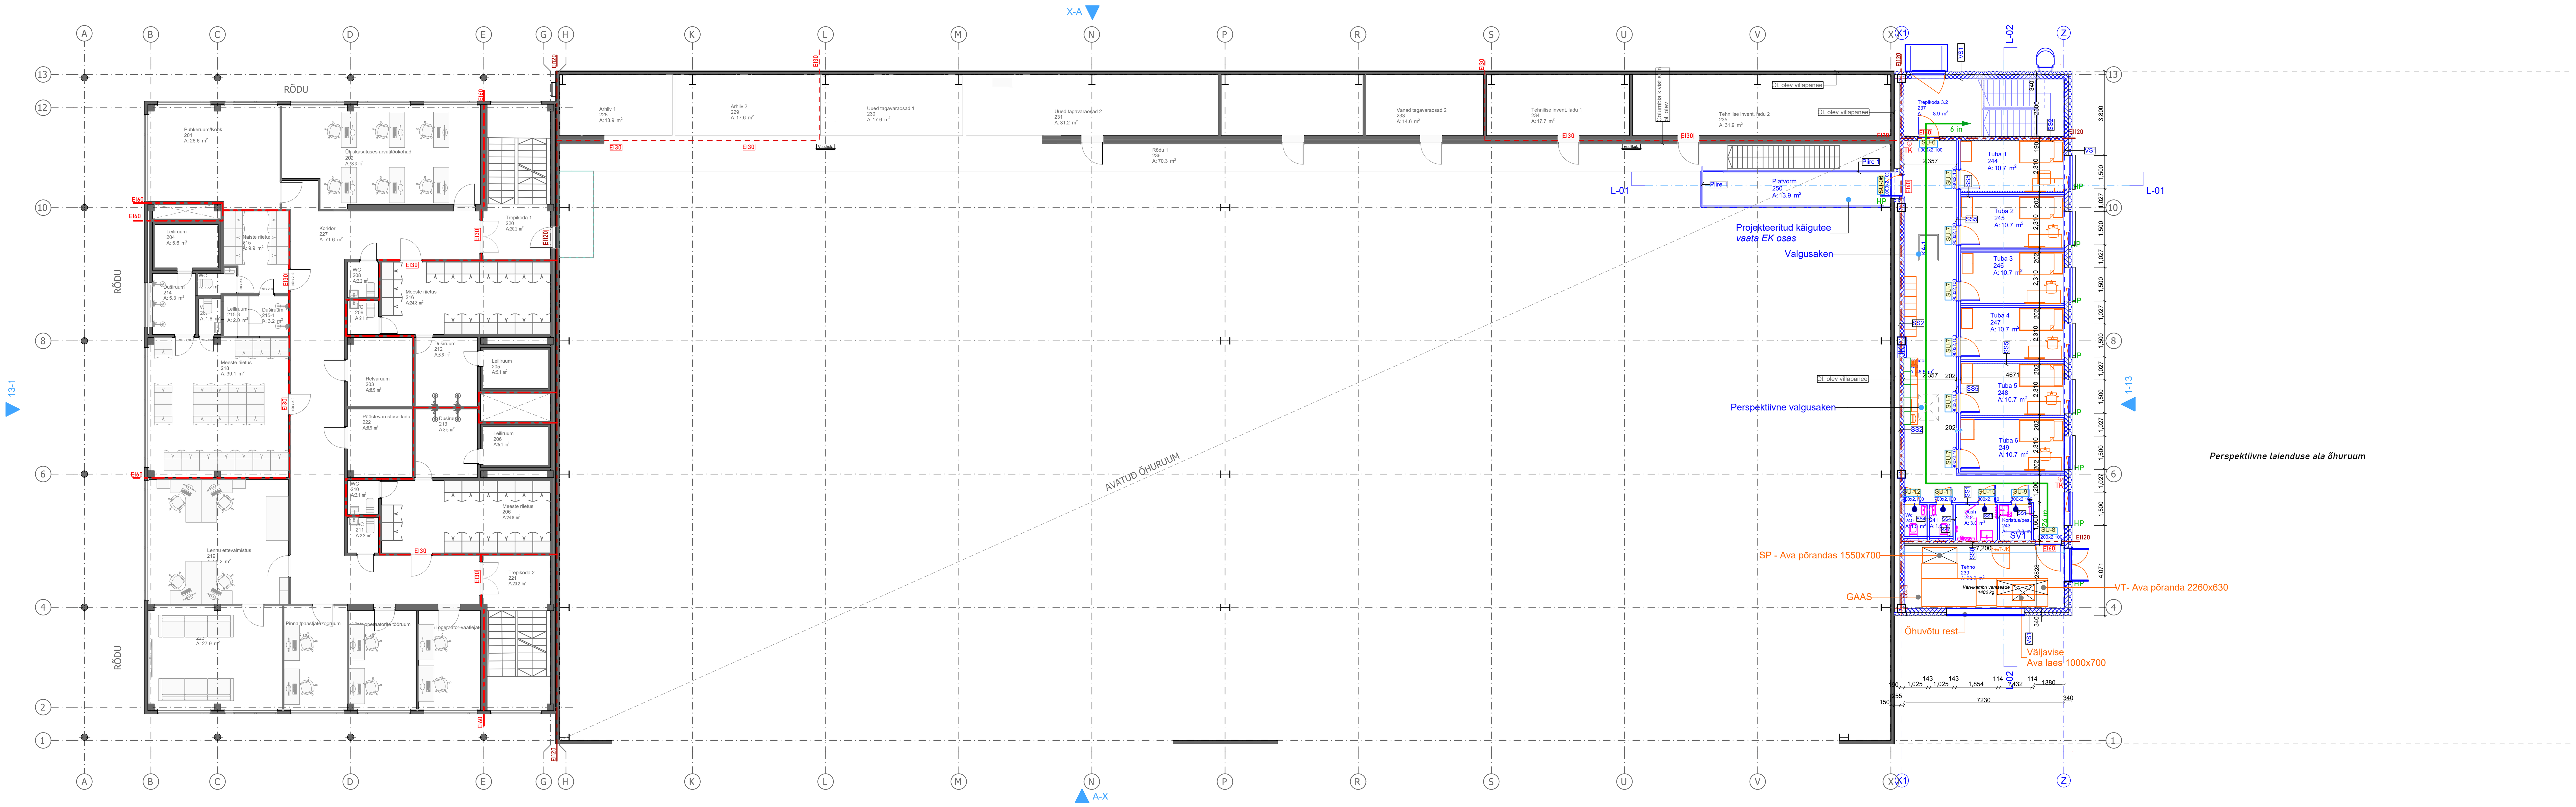

TINGMÄRGID

- EI120 tuletõkkesektsioon
- EI60 tuletõkkesektsioon
- EI30 tuletõkkesektsioon
- EI60 Tuletõkke avatäide *(number näitab tulepüsivust minutites)*
- SS4 Konstruktsioonitüübi tähis
- Planeeritav mööbel/tehnoloogia (lahendatakse eraldi)
- Evakuatsioon / väljumistee
- HP Hädaväljapääs
- TK Tulekustuti asukoht
- GAAS Gaasimõõte sõlm
- SV1/2 Ventilatsiooni seade
- JK Jaotuskilp
- Märgruumi nõuetele vastav sisekliima (materjalide valikul)

Joonist lugeda värvilisena. Joonise värvide põhimõte:

Sinine värvikasutus = uued ja muudetavad lahendused
Hall ja must värvi kasutus = olemasolev olukord

Märkused:
1) Konstruktsioonitüübid on kirjeldatud joonisel AR-8-02 ja EK osas
2) Ruumide eksplikatsioonid on toodud AR-8-01
3) Suitsueemalduse plaan on esitatud eraldi

MÄRKUSED:
Joonise alusena on kasutatud Ehitusinsener OÜ (reg 12481341) poolt koostatud Lennutehnika angaari laiendamise ehitusprojekti (töö nr 24048) PP staadiumis jooniseid.

ASUTUSESISESEKS KASUTAMISEKS:
Märge tehtud: 06.03.2025
Kehtib kuni: 06.03.2030
Alus: AvTS § 35 lg 1 p 9, 10
Teabevaldaja: Politsei- ja Piirivalveamet

RESHAPE.

RESHAPE OÜ | rg-kood 16246878 | www.reshape.ee | info@reshape.ee

PROJEKT: LENNUTEHNIKA ANGAARI LAIENDAMINE
AADRESS: VÄIKE-SÕJAMÄE 22A, LASNAMÄE, TALLINN, HARJU MAAKOND
TELLIJA: RIIGI KINNISVARA AS
ARHITEKTID: SAAMUEL RAMMO
VASTUTAV ARHITEKT: TAURI TAMME
JOONIS: 2. KORRUS
STAADIUM: TÖÖPROJEKT
FORMAAT: 594x841
TÖÖ NR.: A05032501
KUUPÄEV: 15/03/2025
MÕÕTKAVA: 1:150
JOONISE NR.: AR-5-02